
 
 
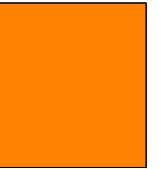
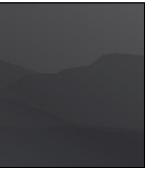
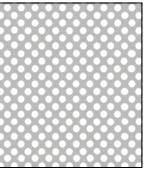
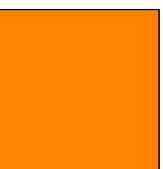
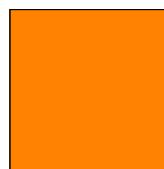
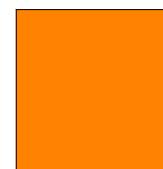
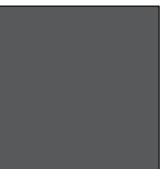
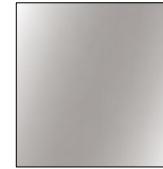
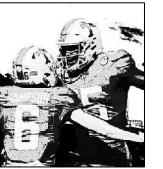
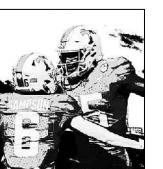


PAINT	ACRYLIC PAINT	LAMINATE	VINYL	GRAPHIC	PERF
P1  WHITE	A1  WHITE MATTHEWS PAINT MP27386 VERIZON WHITE	L1  HIGH GLOSS WHITE ABET LAMINATE LUCIDA - 405	V1  ORANGE VINYL FOR LIT SIGNAGE: ORACAL 8300 COLOR 20 - GOLDEN YELLOW	WC1  WALLCOVERING GRAPHIC	PF1  PERF METAL MCNICHOLS PERFORATED METAL ROUND, ALUMINUM, ALLOY 3003-H14, .1250" THICK (8 GAUGE), 1" ROUND ON 1-1/4" STAGGERED CENTERS
P2  ORANGE	A2  ORANGE MATTHEWS PAINT PMS 151 CLEAR ACRYLIC SATIN FINISH	L2  ORANGE WILSONART ORANGE GROVE D501-01 HIGH GLOSS WILSONART MATTE NATURAL 6252		G1  FABRIC GRAPHIC	
P3  SMOKEY GRAY MATCH PMS COOL GRAY II	A3  SMOKEY GRAY MATCH PMS COOL GRAY II	L3  DARK GRAY HIGH GLOSS		G2  BACKLIT FABRIC GRAPHIC	
	A4  DARK GRAY	L4  WILSONART MATTE NATURAL 6252		G3  2ND SURFACE ACRYLIC GRAPHIC PANEL	
		L5  WILSONART POLISHED NATURAL ALUMINUM 6251		G4  PRINTED VINYL GRAPHIC	

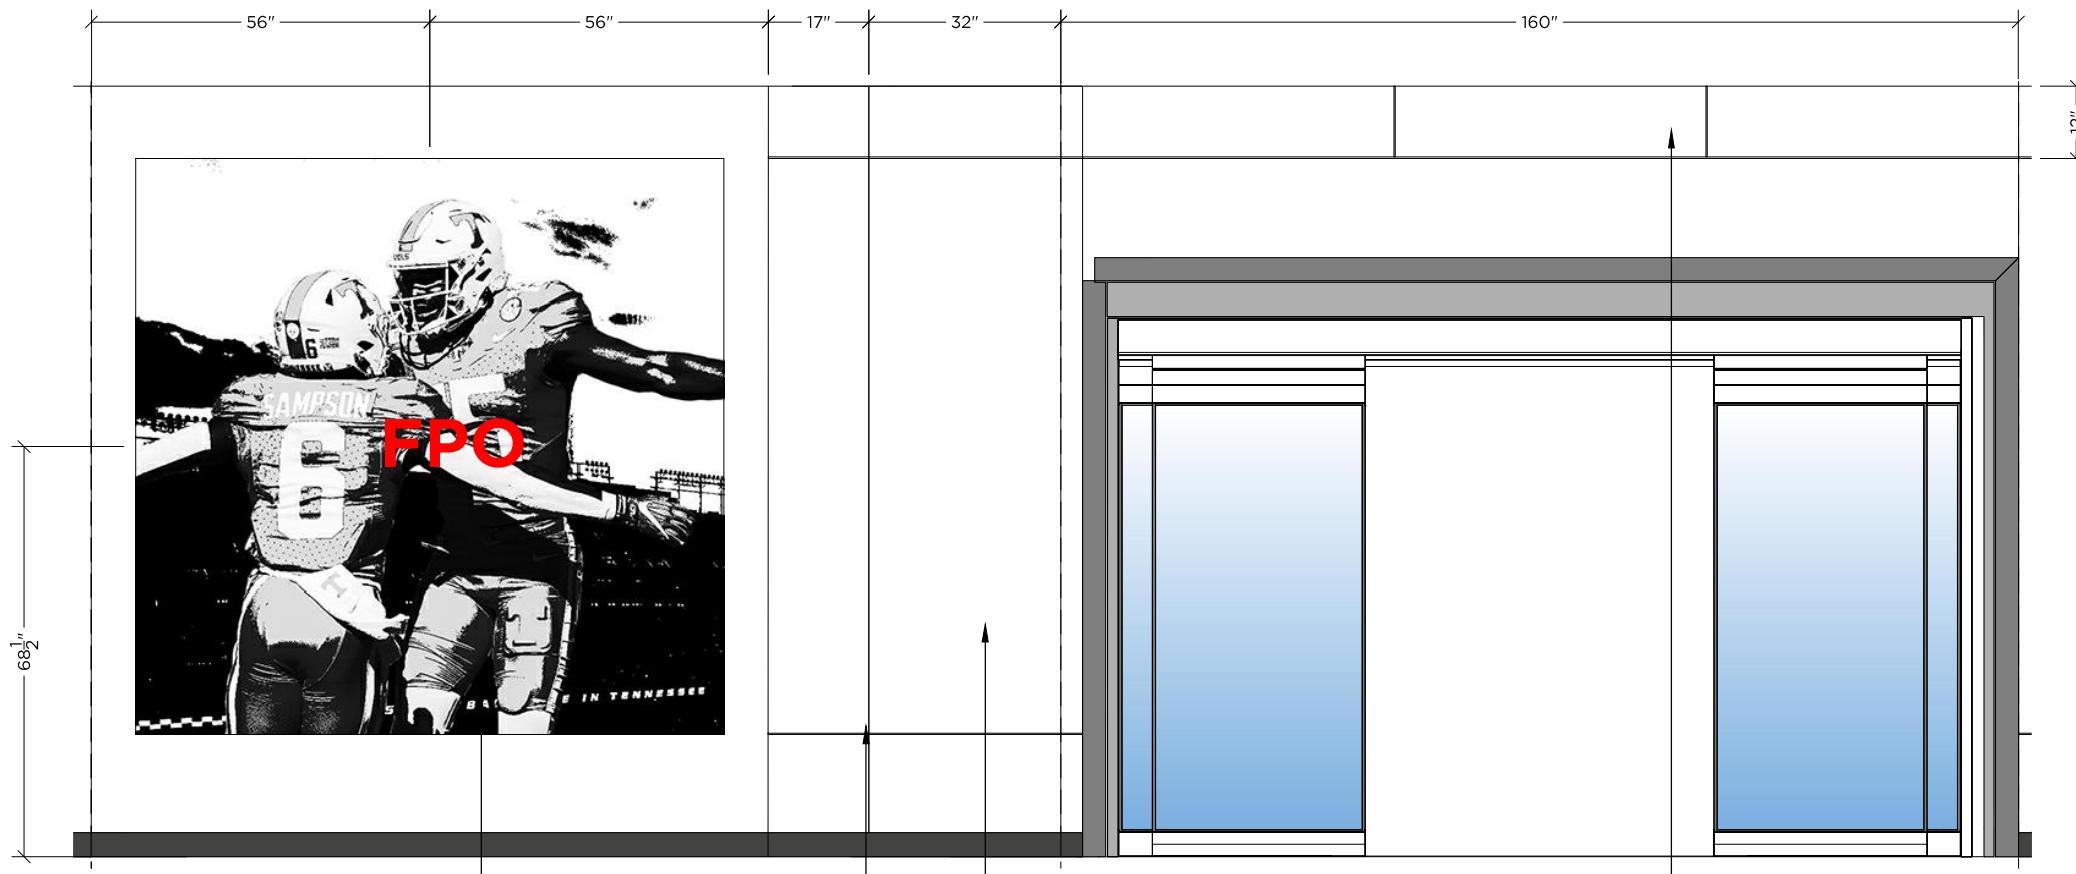

1.1.2 FABRIC GRAPHIC


L1 MILLWORK BUILDOUT




L1 MILLWORK PANELS


**L1 PANELS ANGLED
RETURN LINE BACK
TO WALL**

1 **LOWER ATRIUM - NORTH**
SCALE: 3/8" = 1'-0"




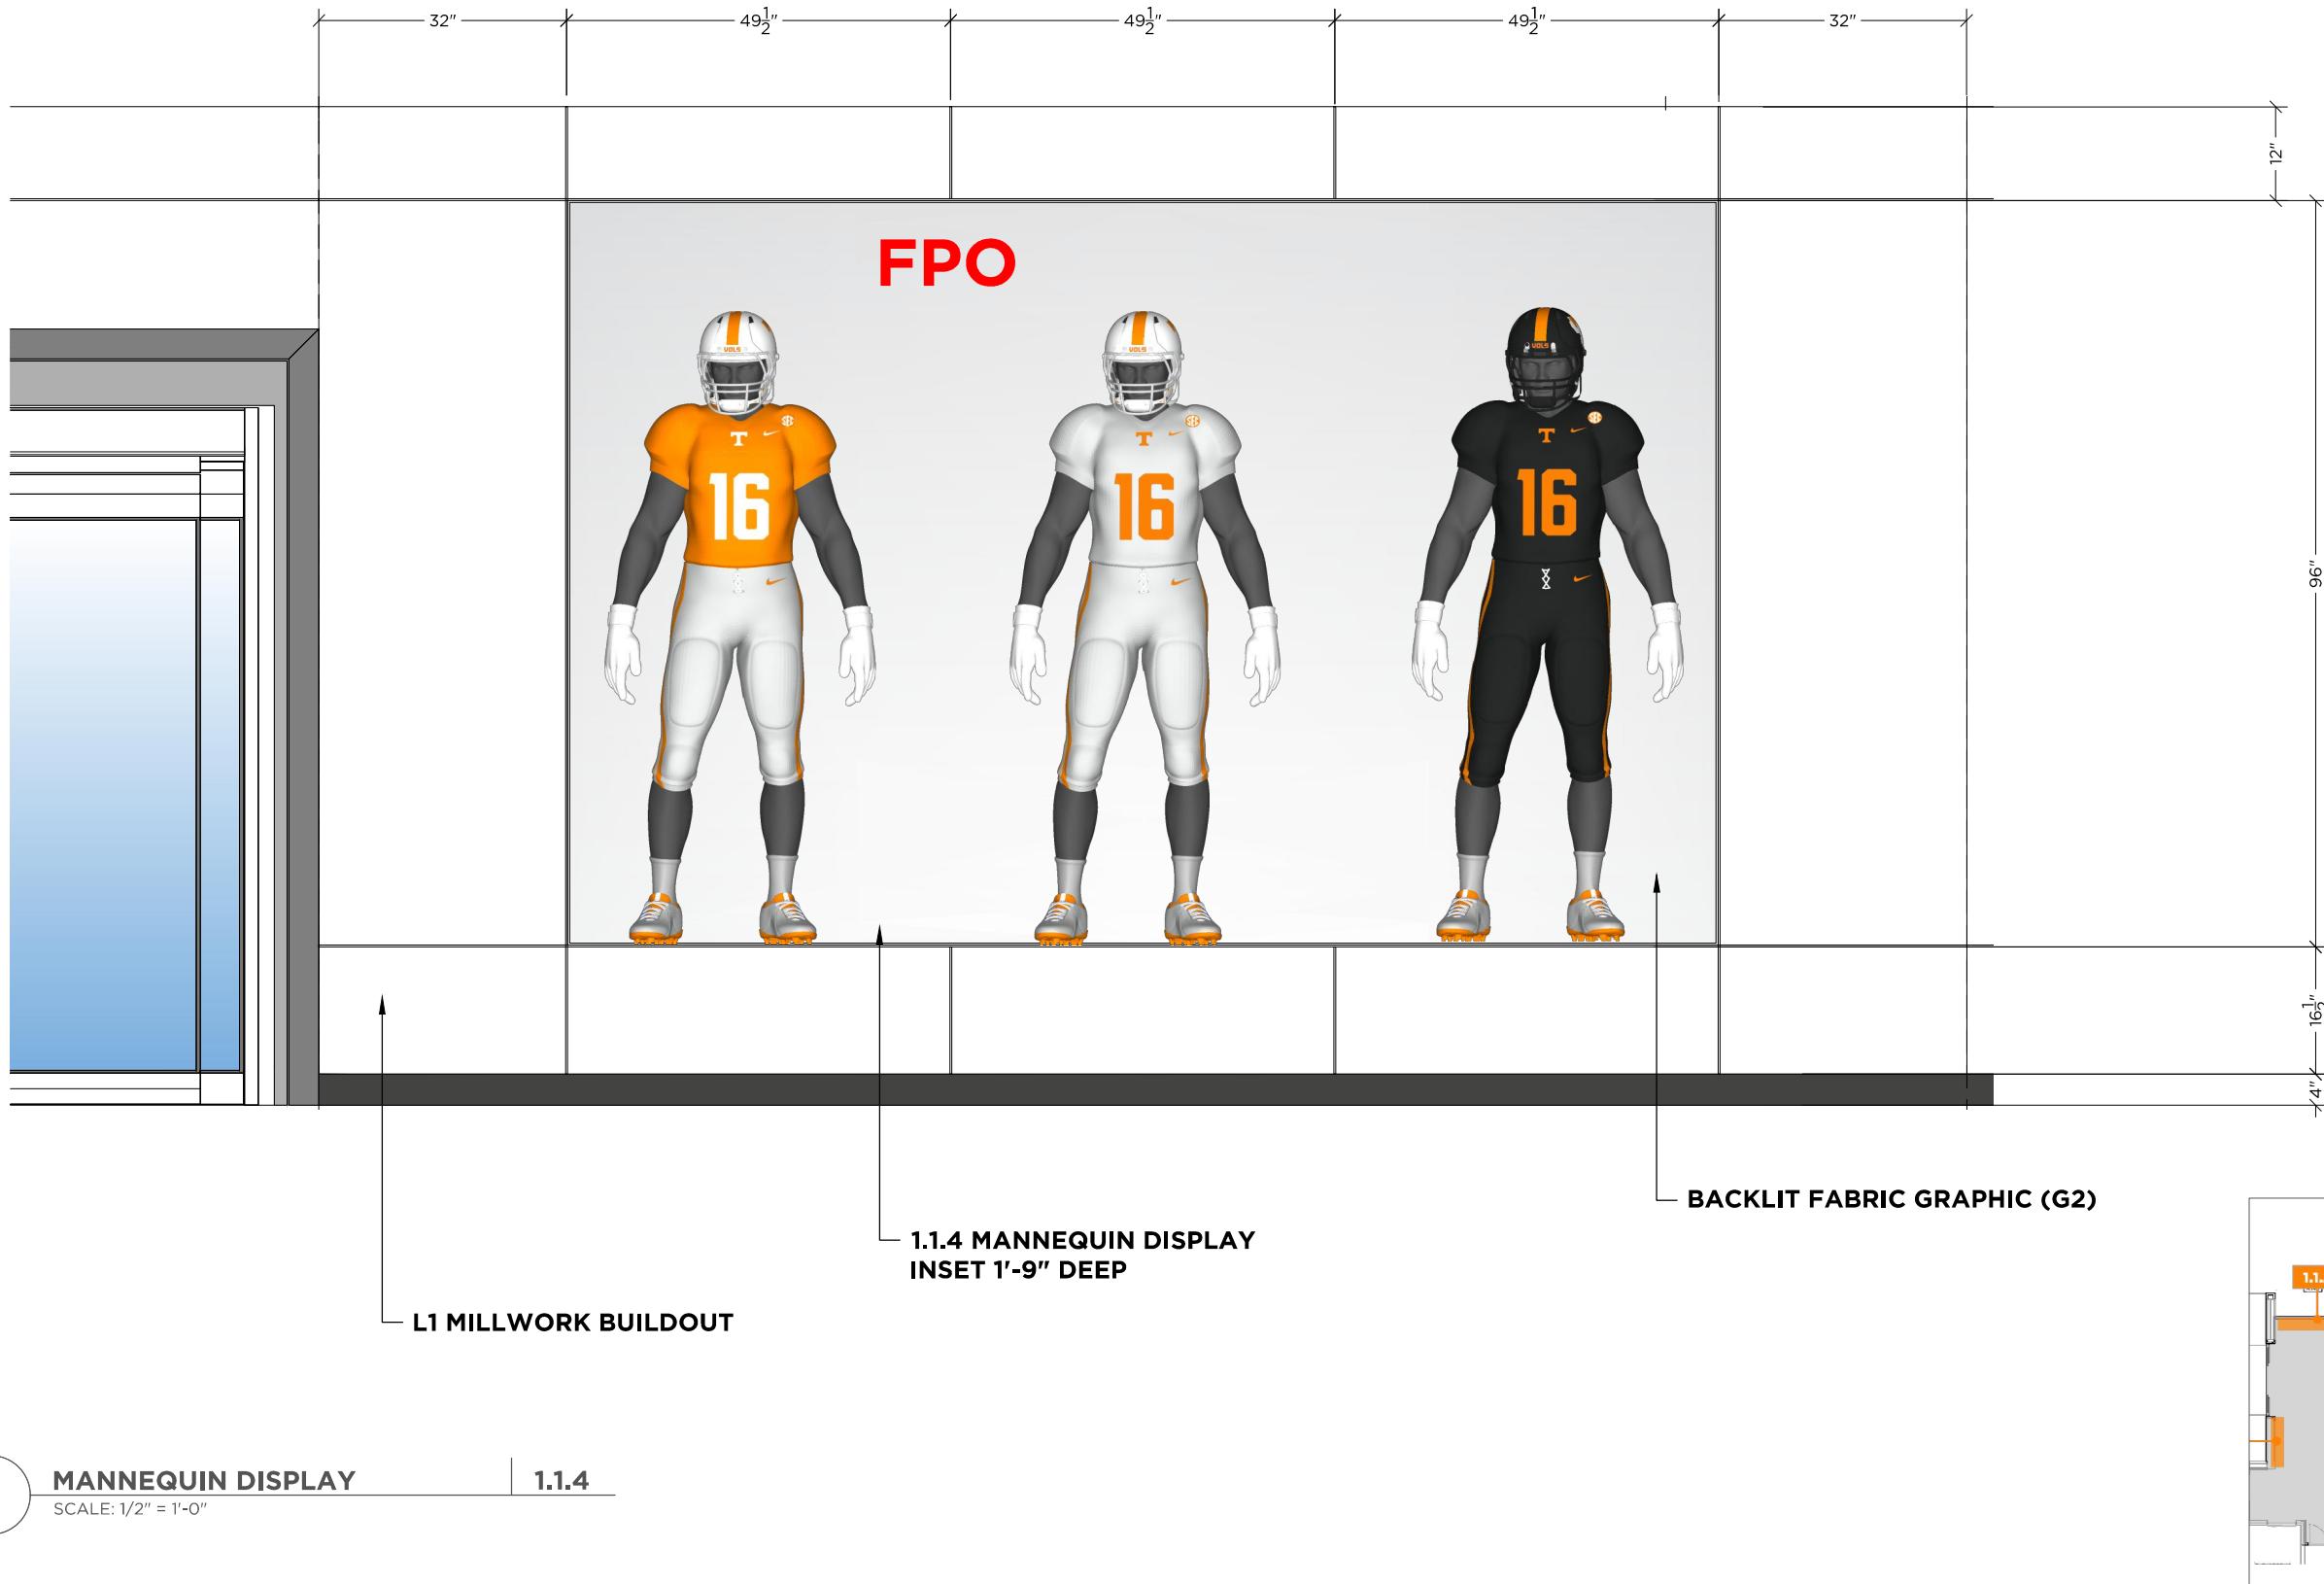


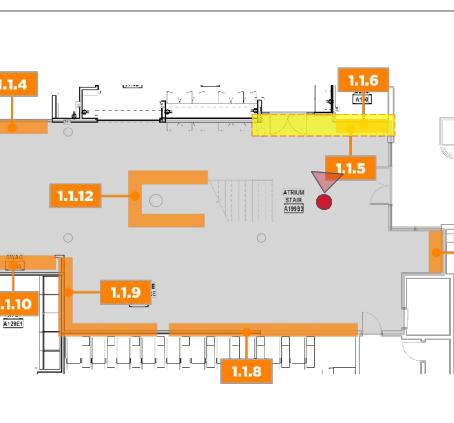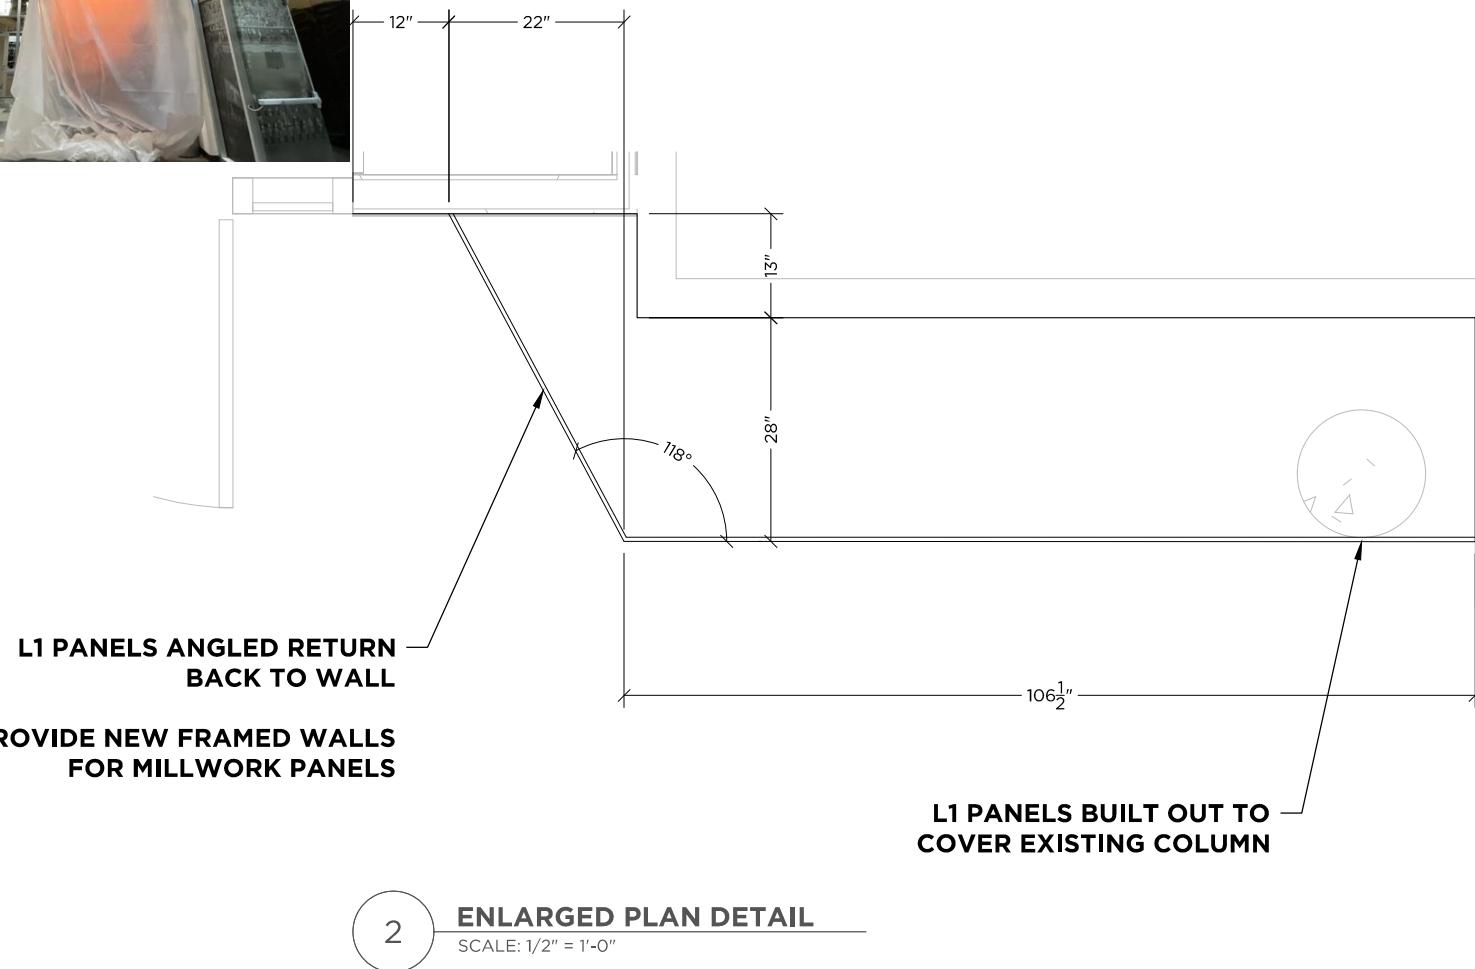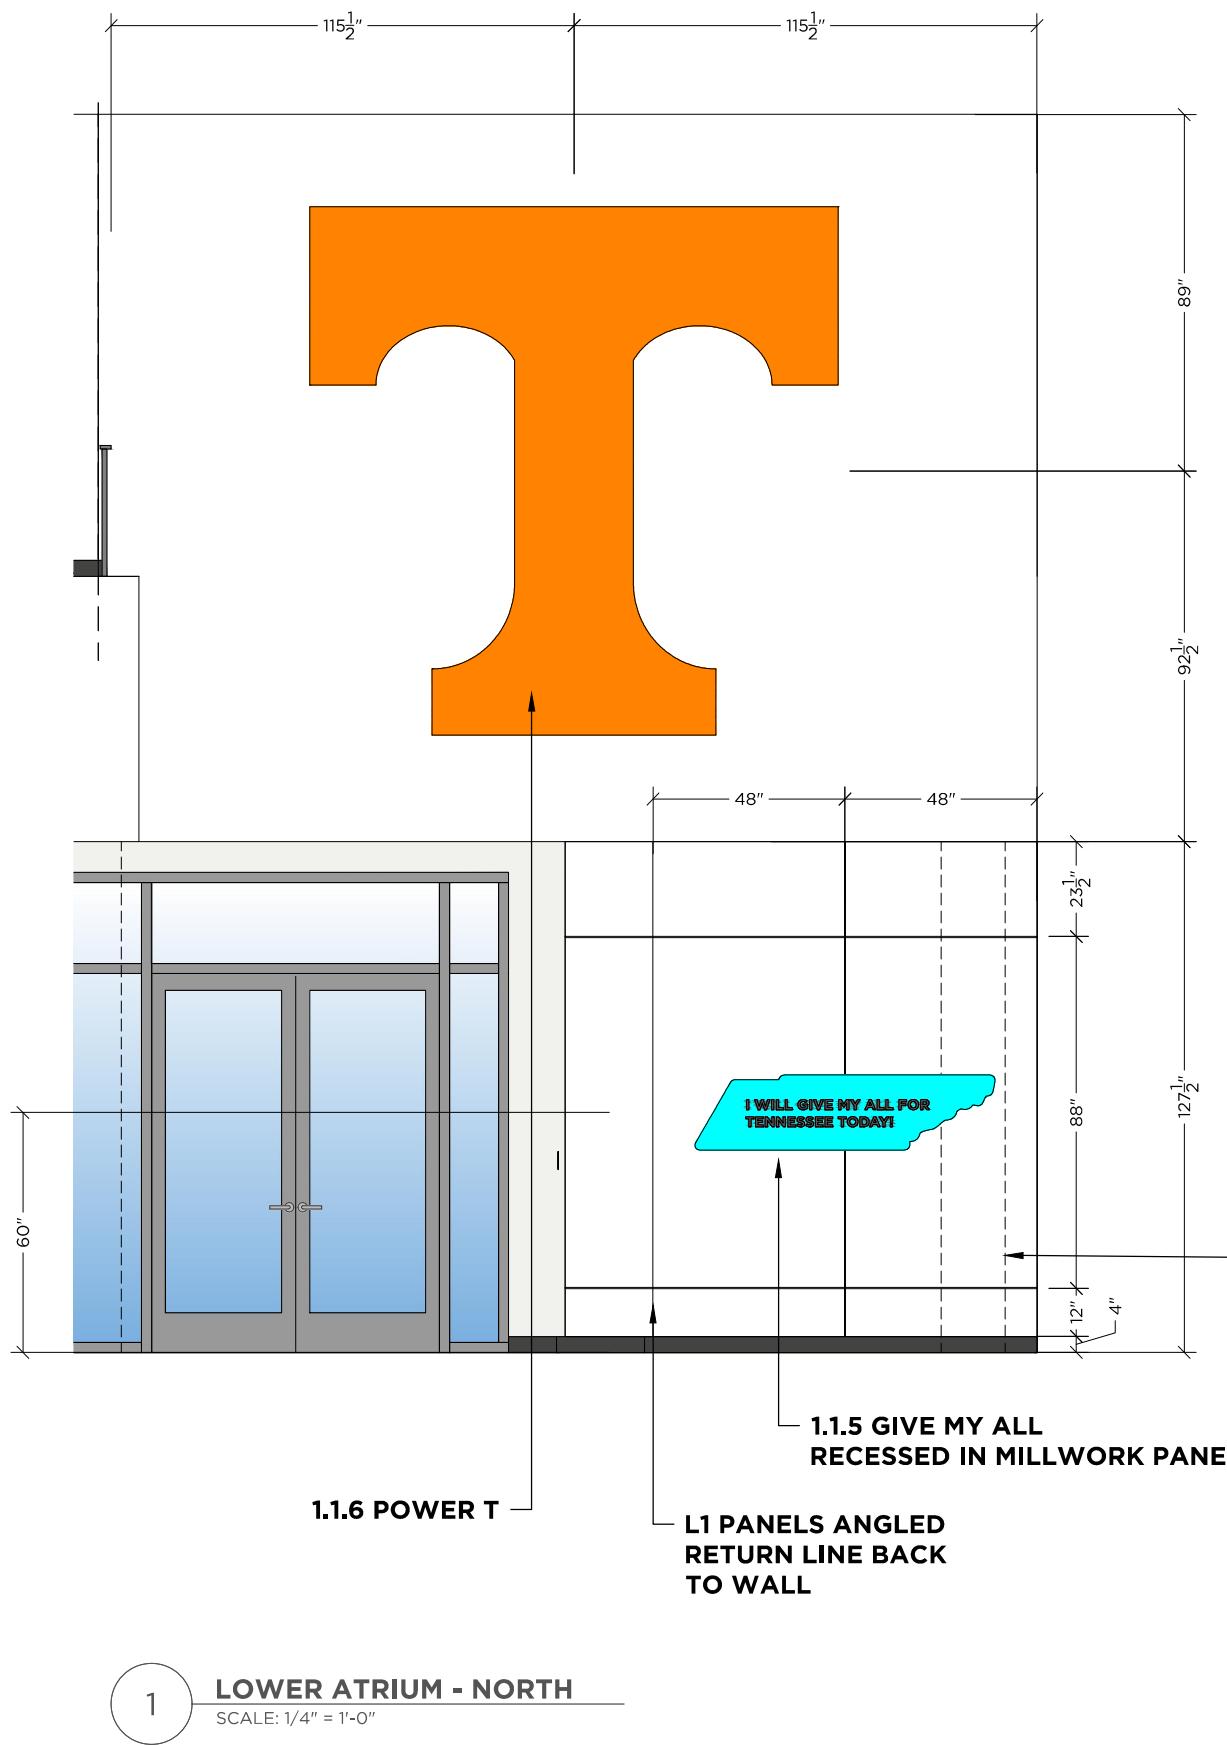

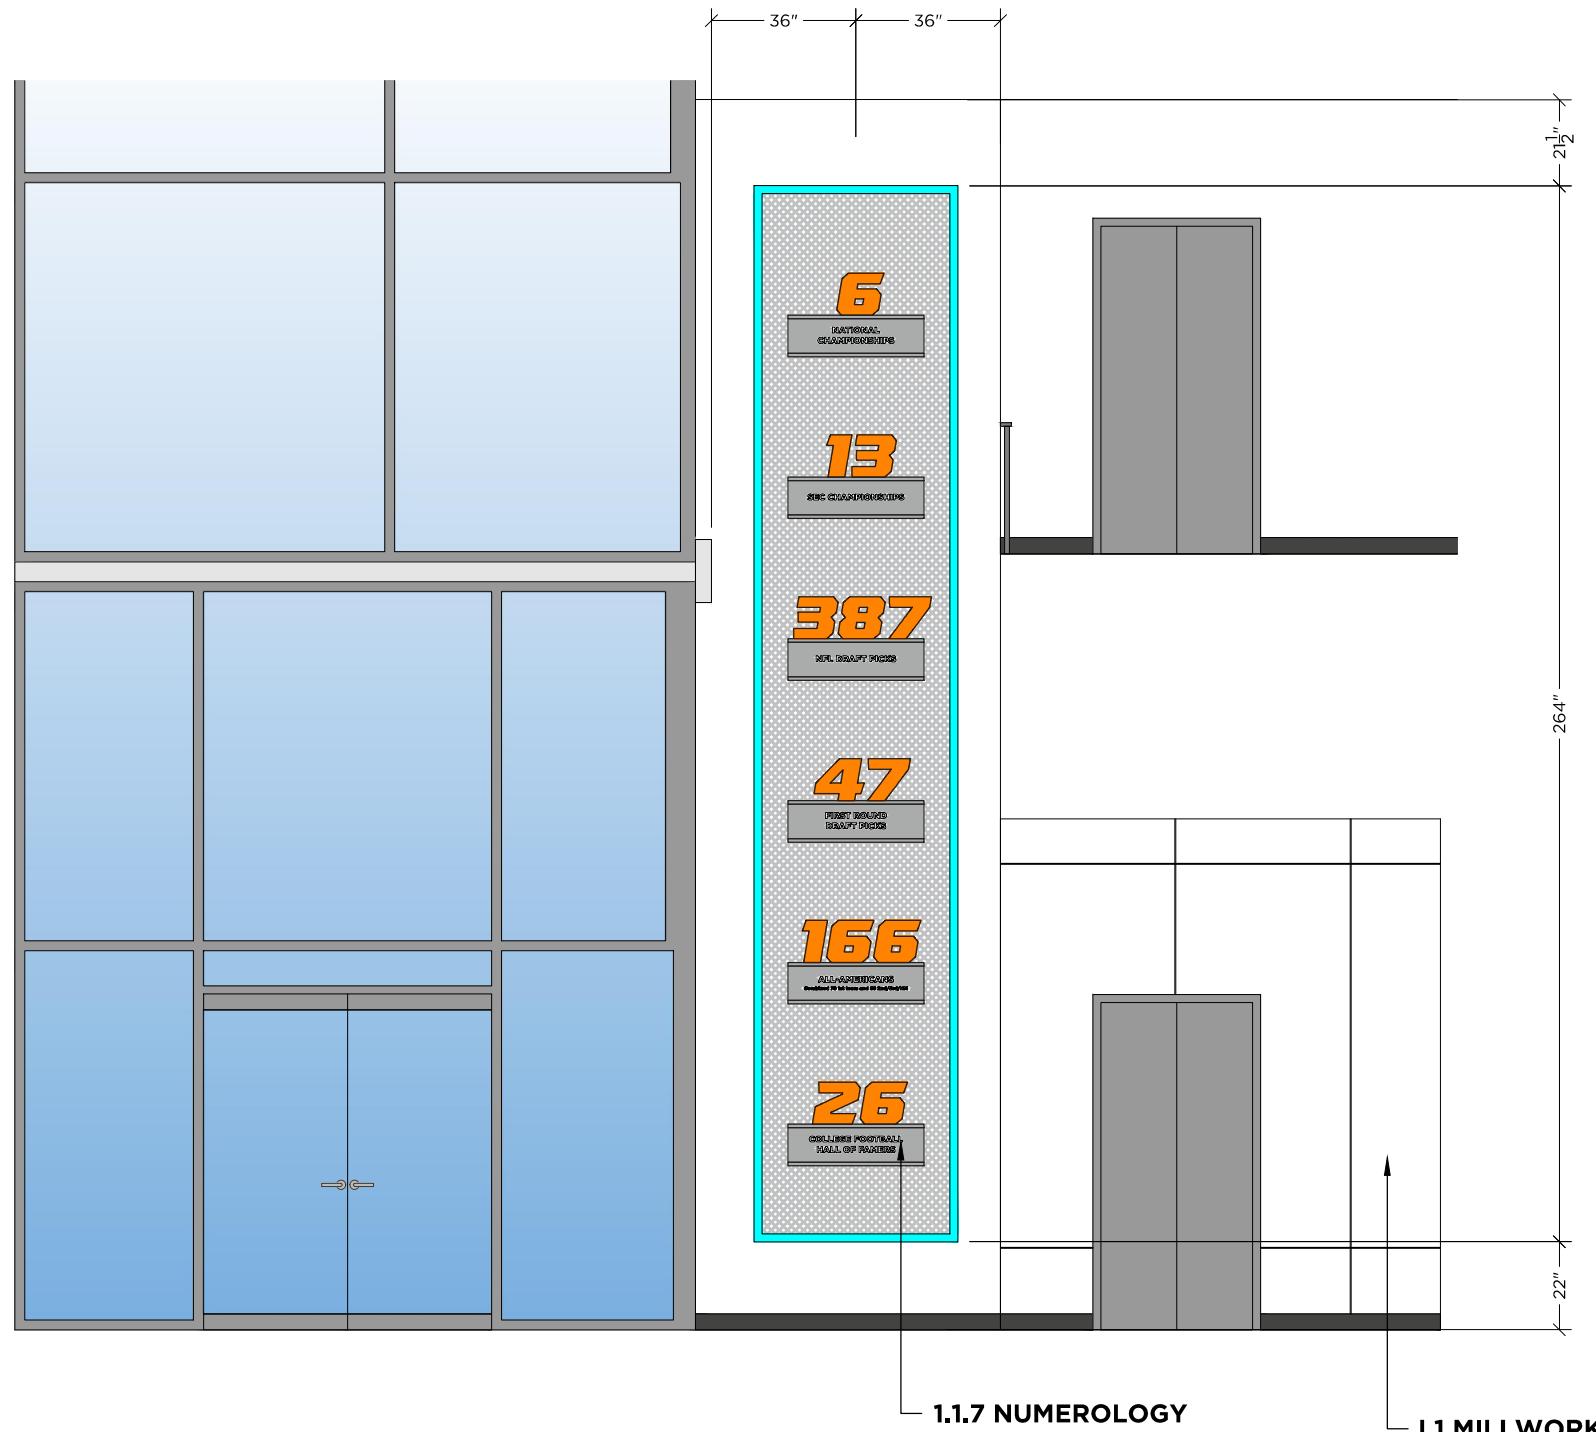


1 LOWER ATRIUM - EAST
SCALE: 1/4" = 1'-0"

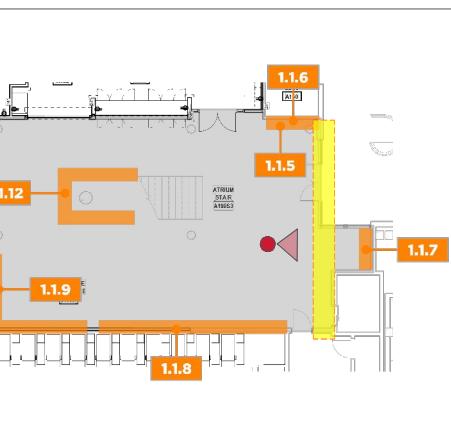

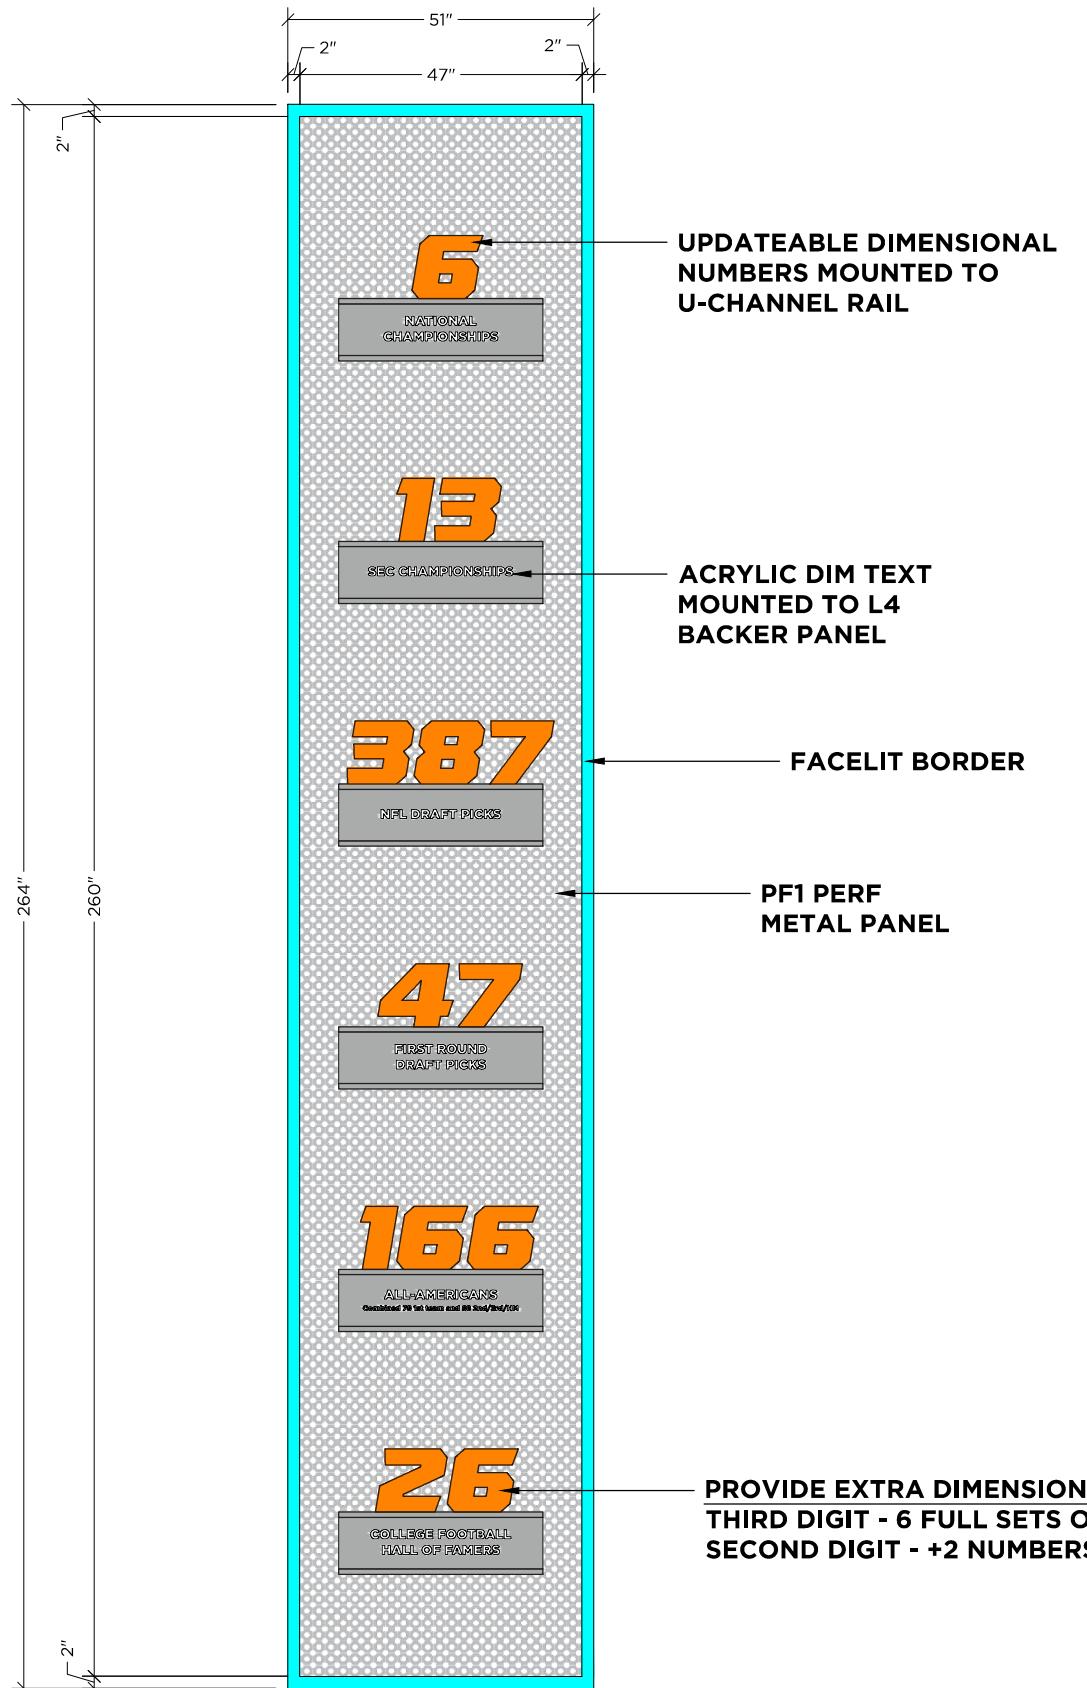


**PROVIDE EXTRA DIMENSIONAL NUMBERS FOR UPDATEABILITY:
THIRD DIGIT - 6 FULL SETS OF 0-9
SECOND DIGIT - +2 NUMBERS (FOR INCREASE)**

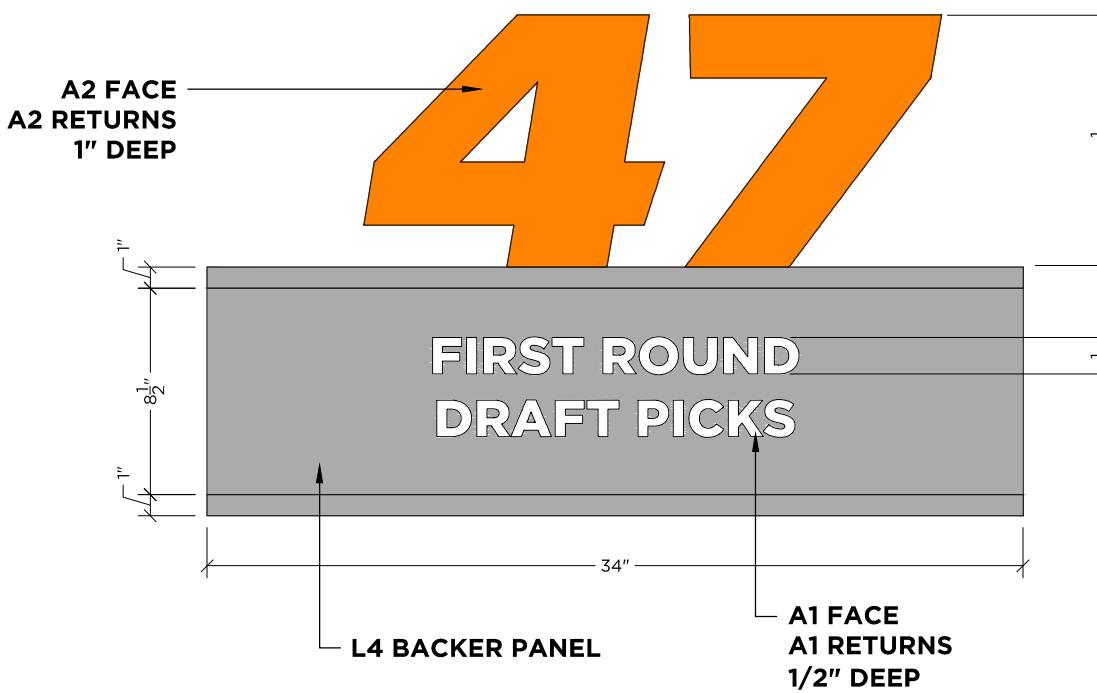



2 NUMEROLOGY DIM TEXT 1.1.7

1 NUMEROLOGY

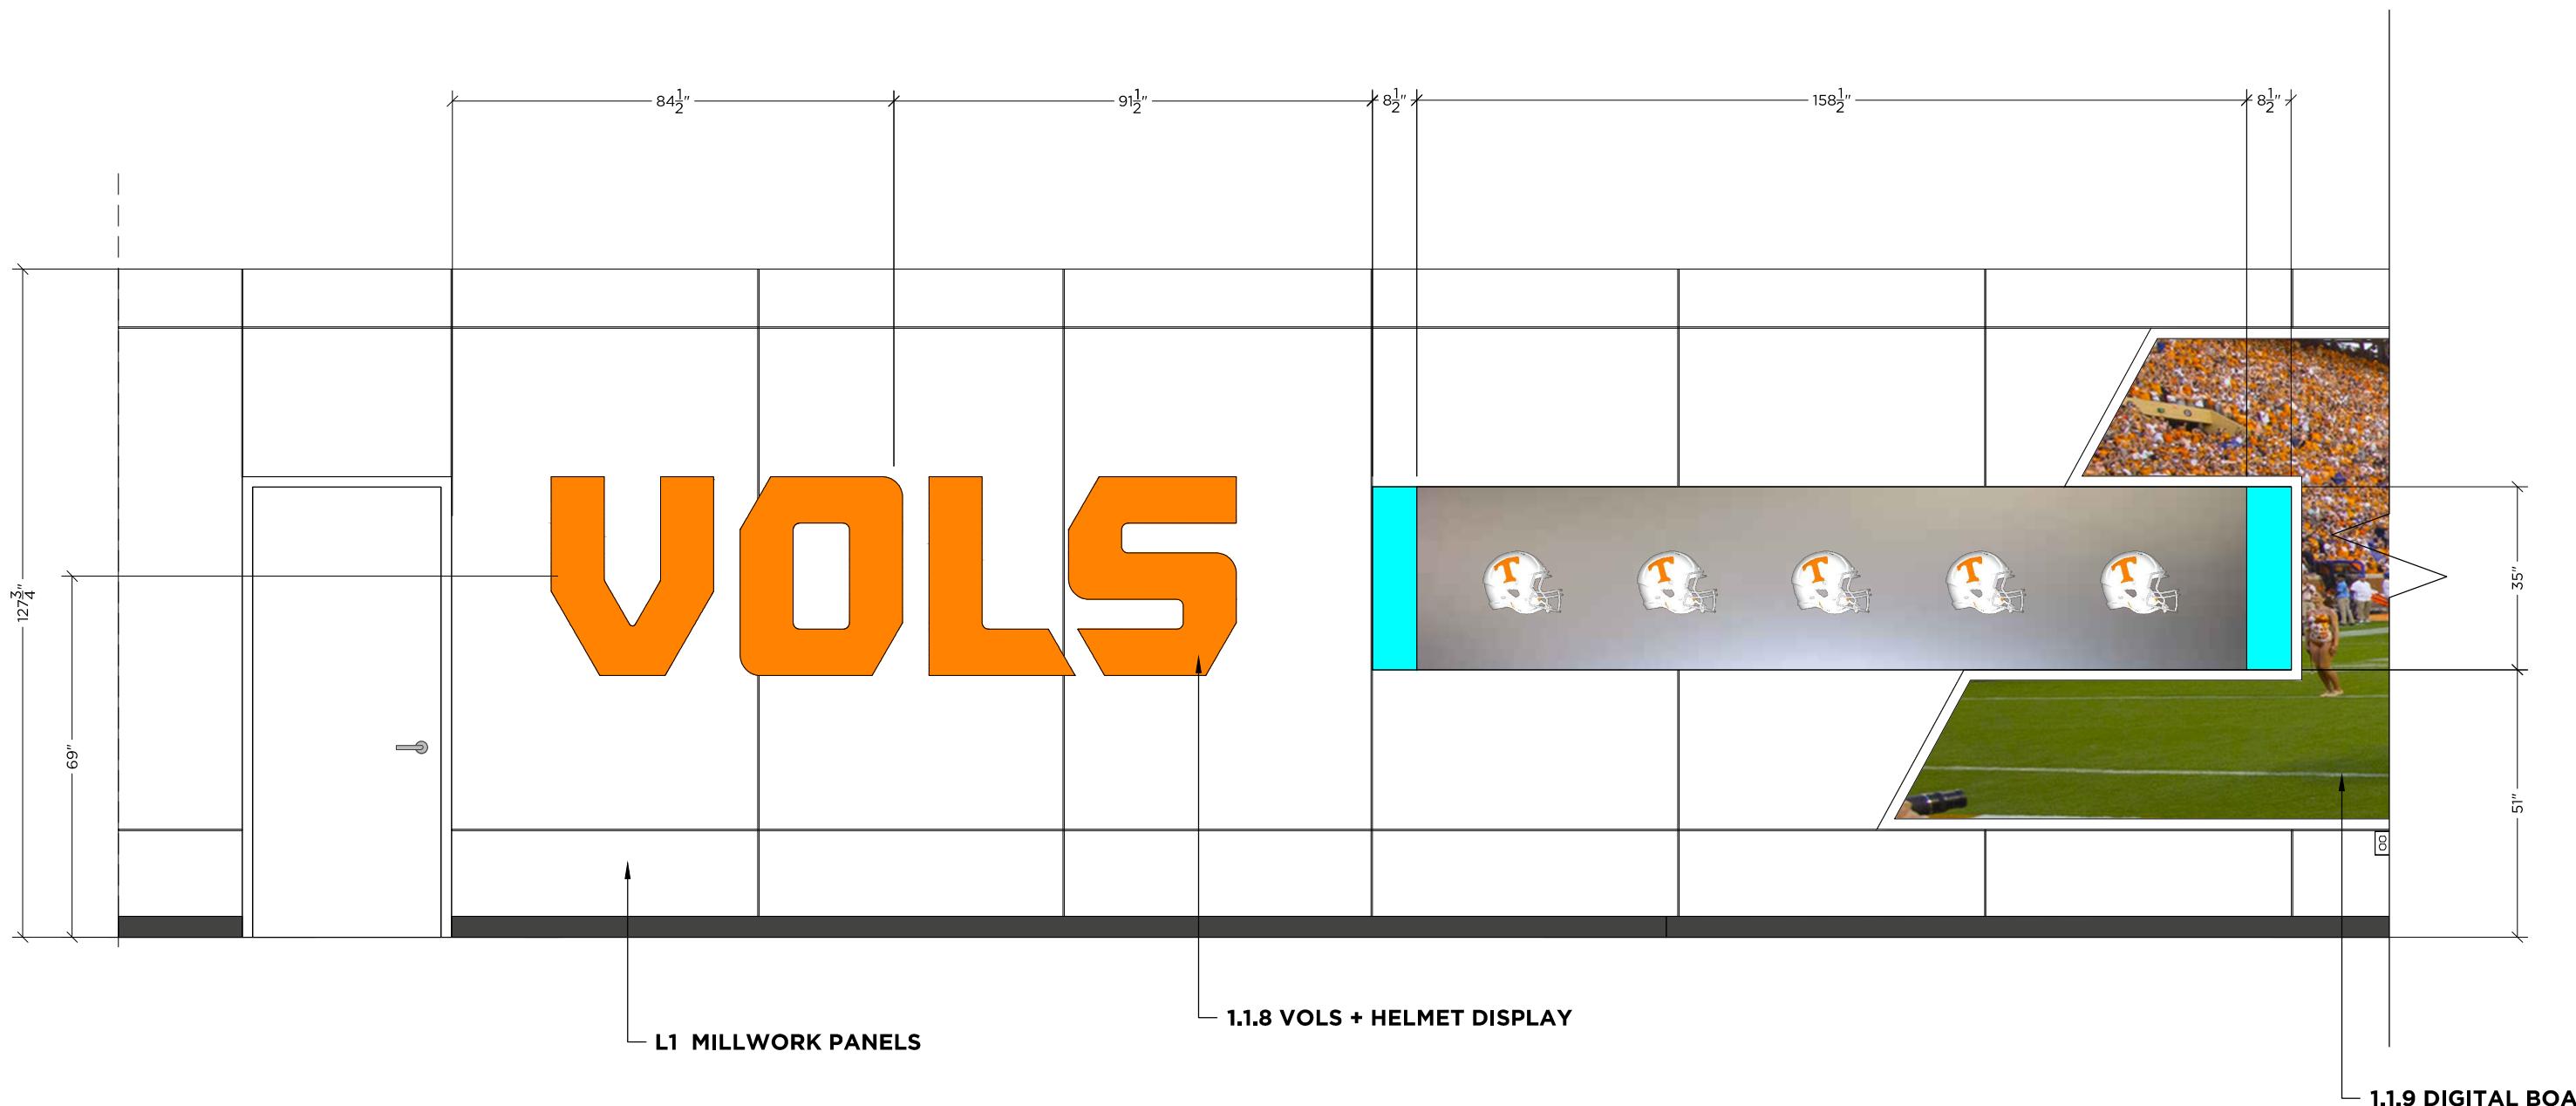



1 VOLS + HELMET DISPLAY 1.1.8
SCALE: 3/8" = 1'-0"

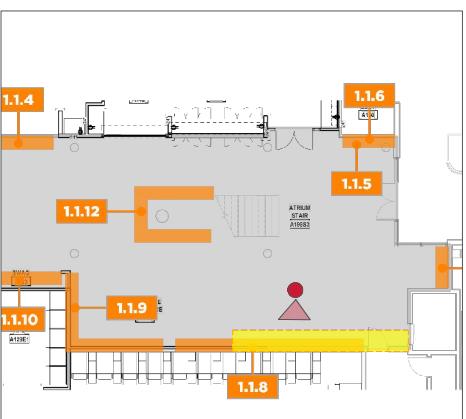

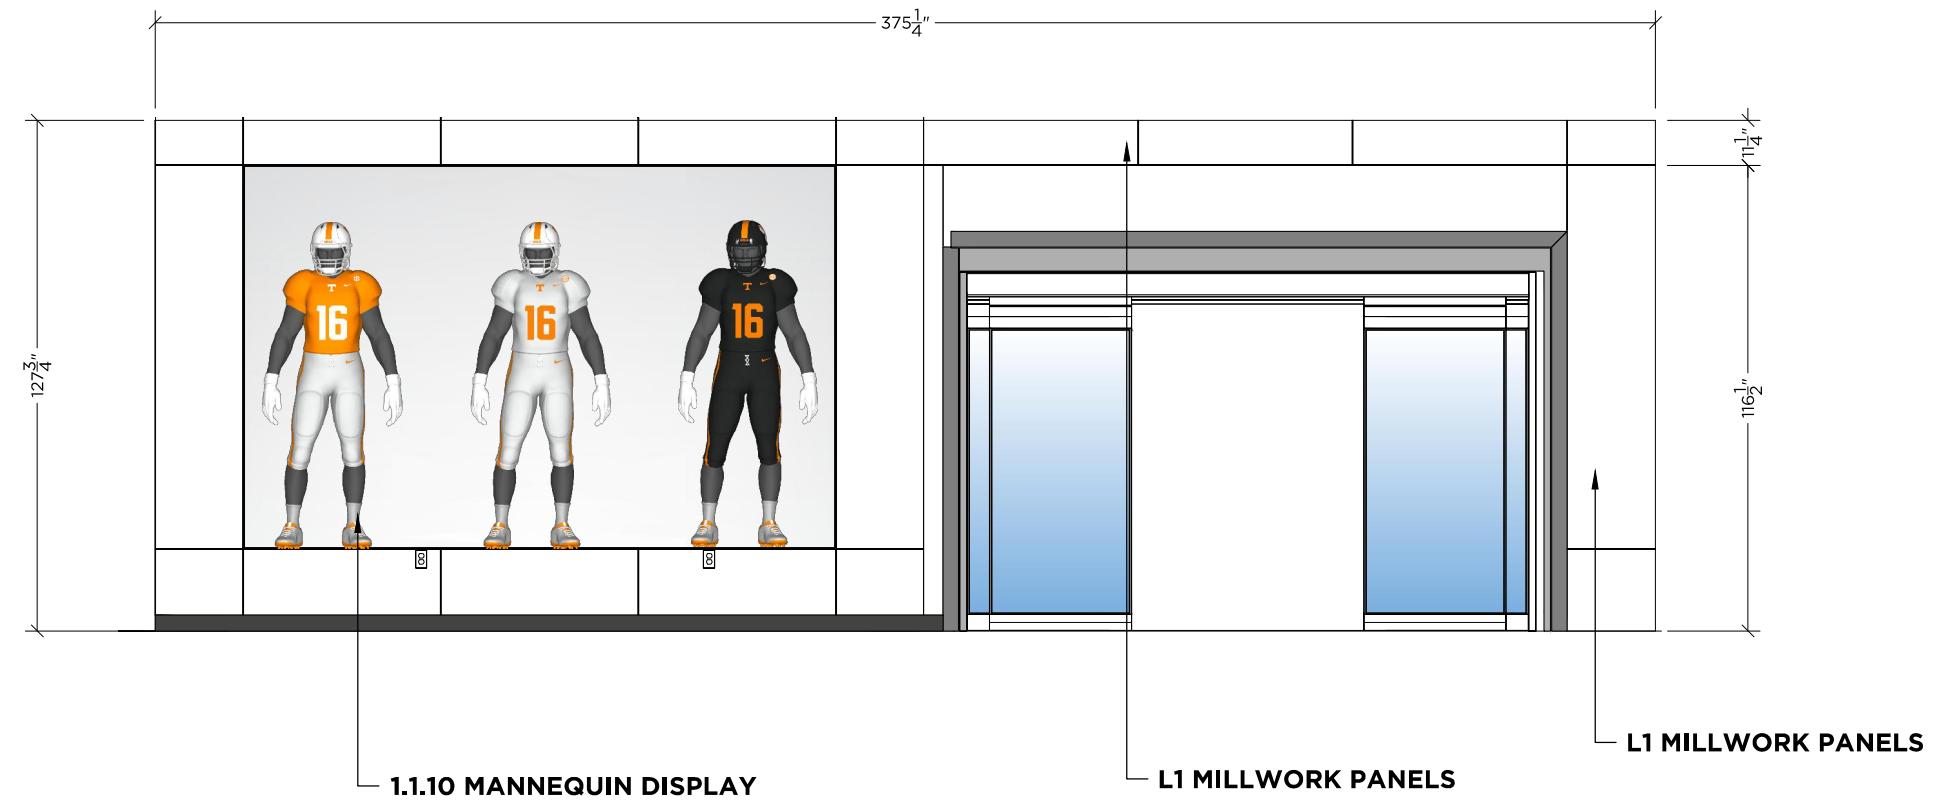



1 **LOWER ATRIUM - SOUTH**
SCALE: 1/4" = 1'-0"

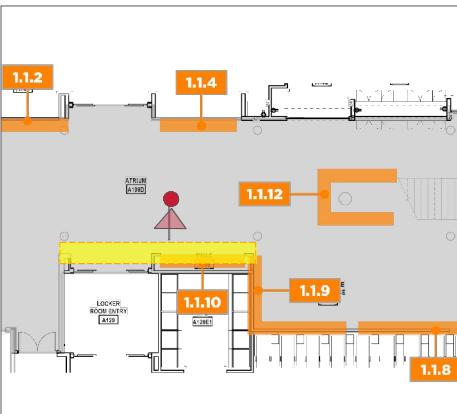

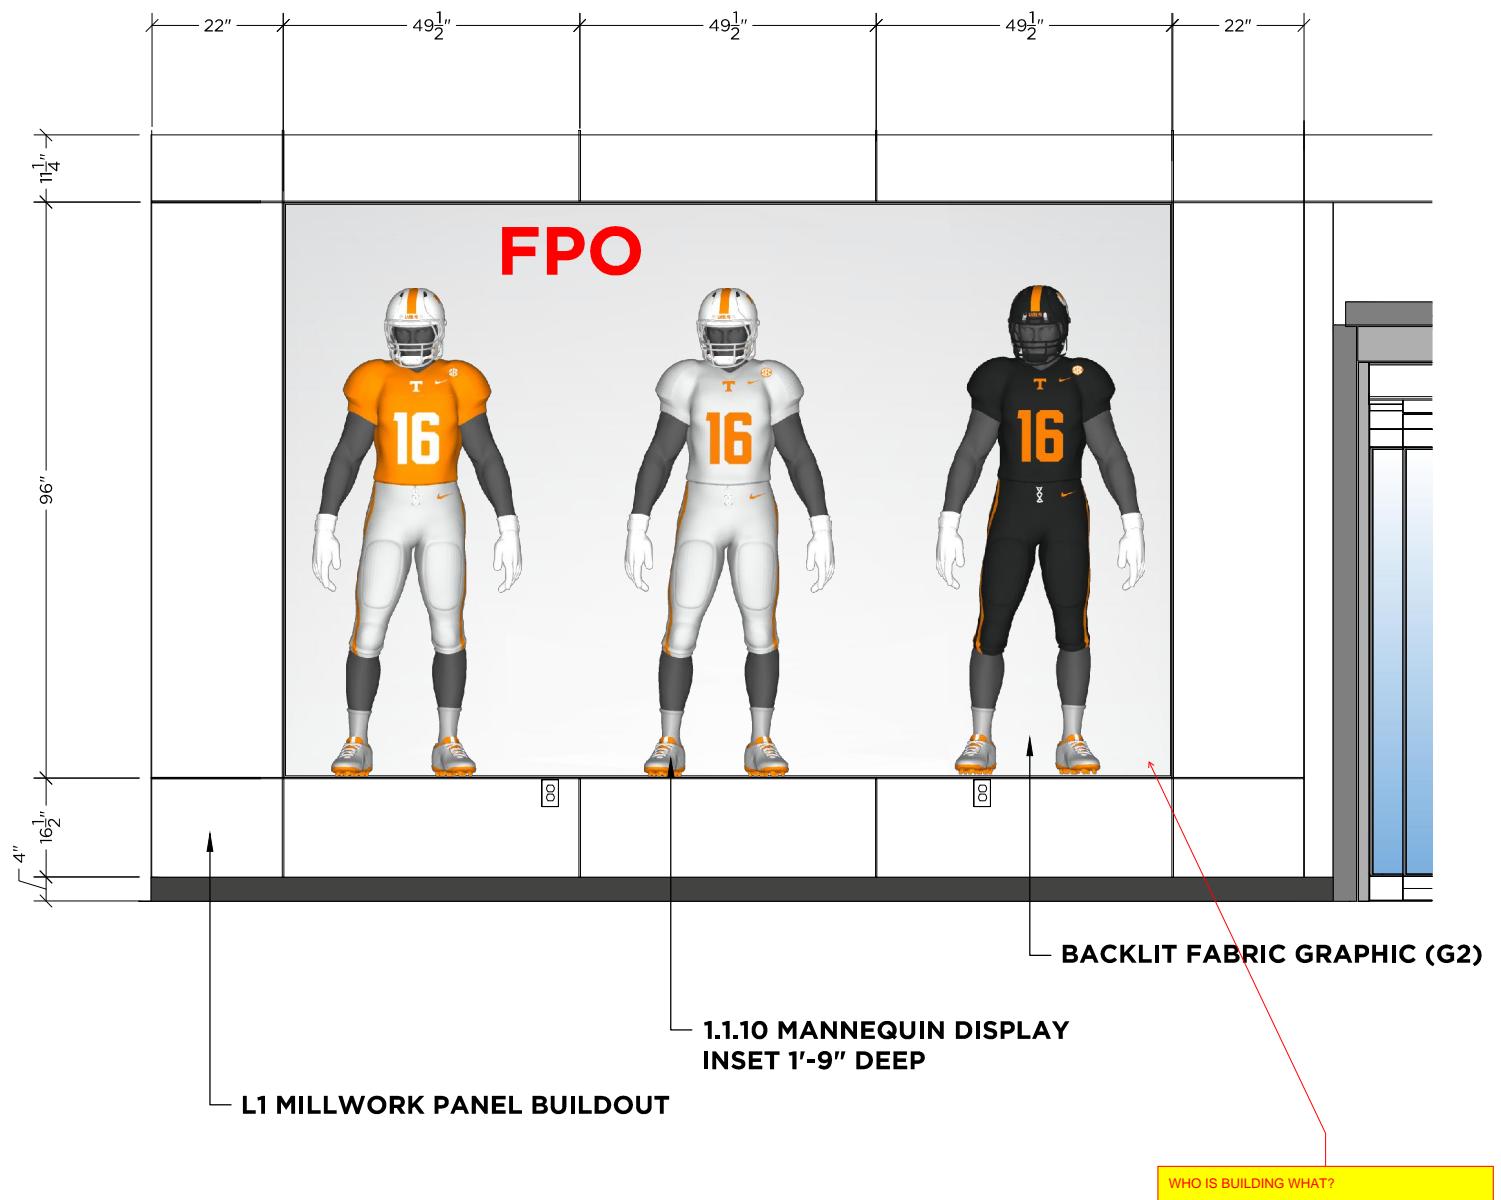


1 MANNEQUIN DISPLAY 1.1.10
SCALE: 3/8" = 1'-0"

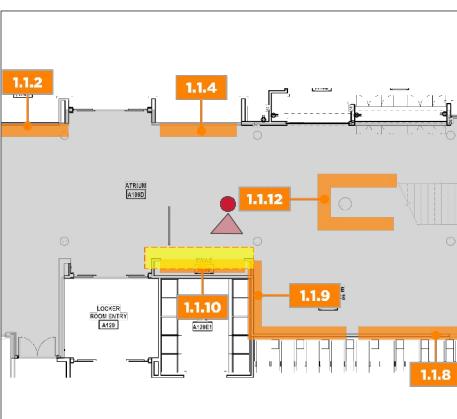


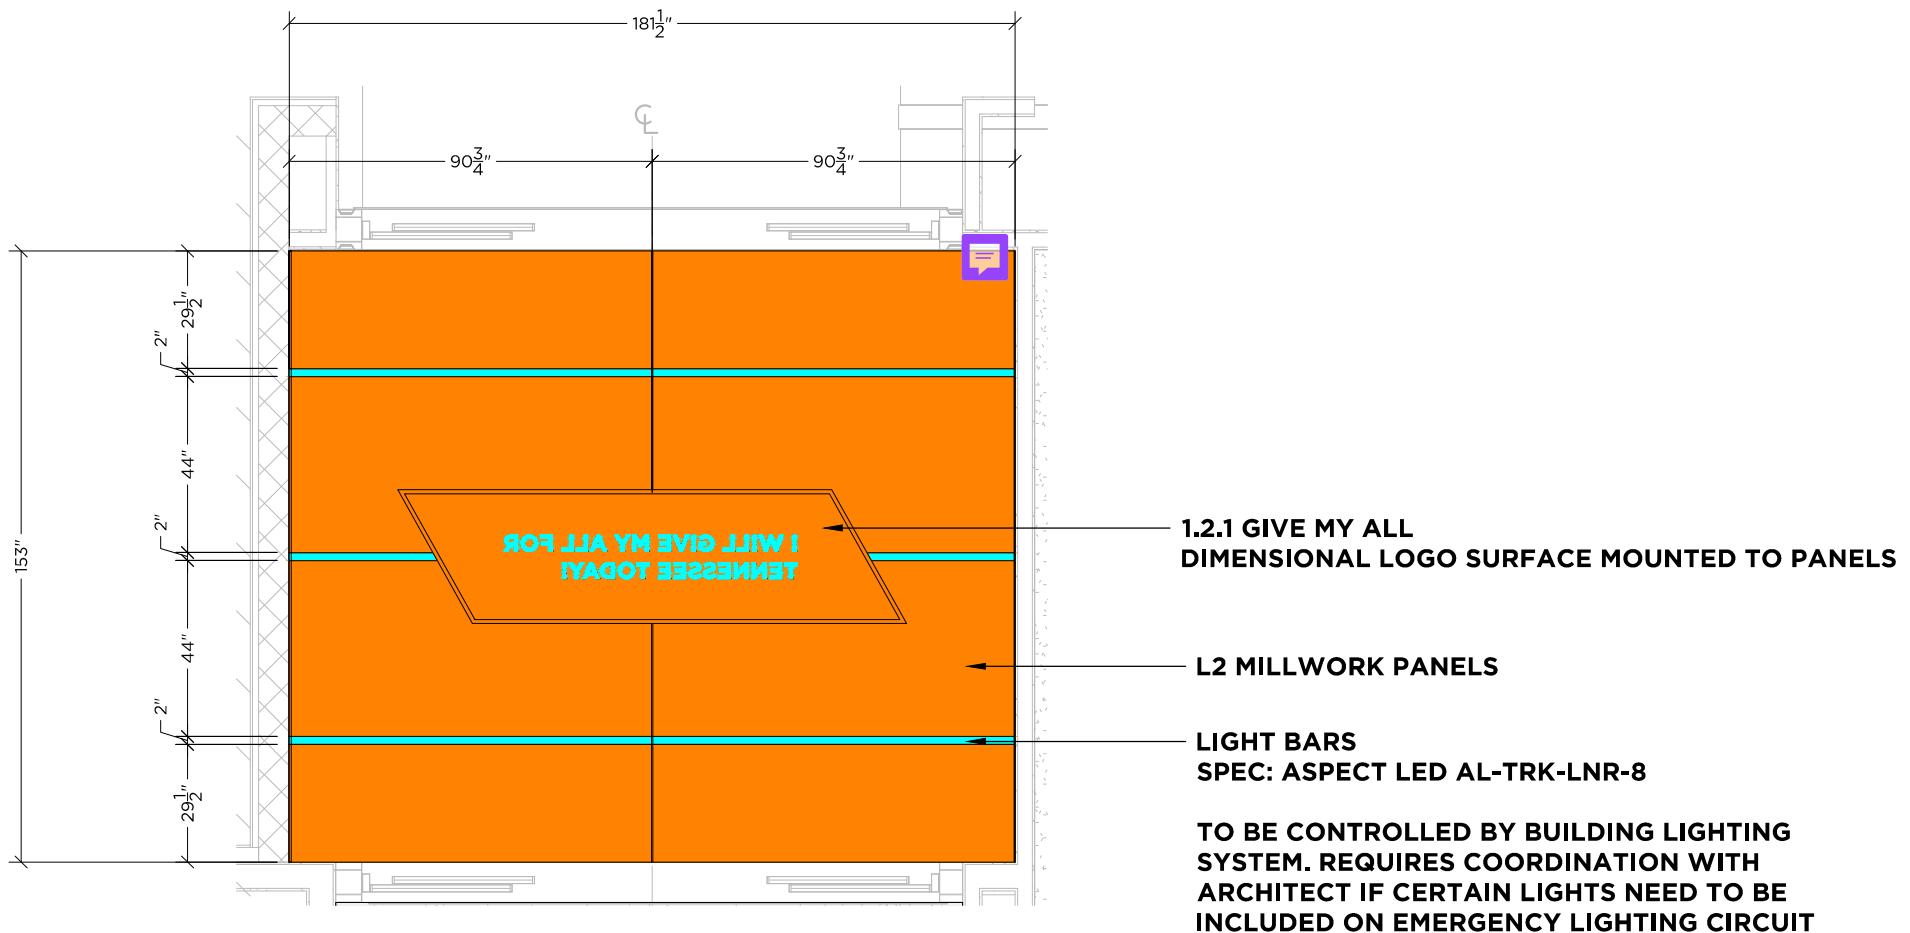


1 LOCKER ENTRY RCP | 1.2.1
SCALE: 1/4" = 1'-0"

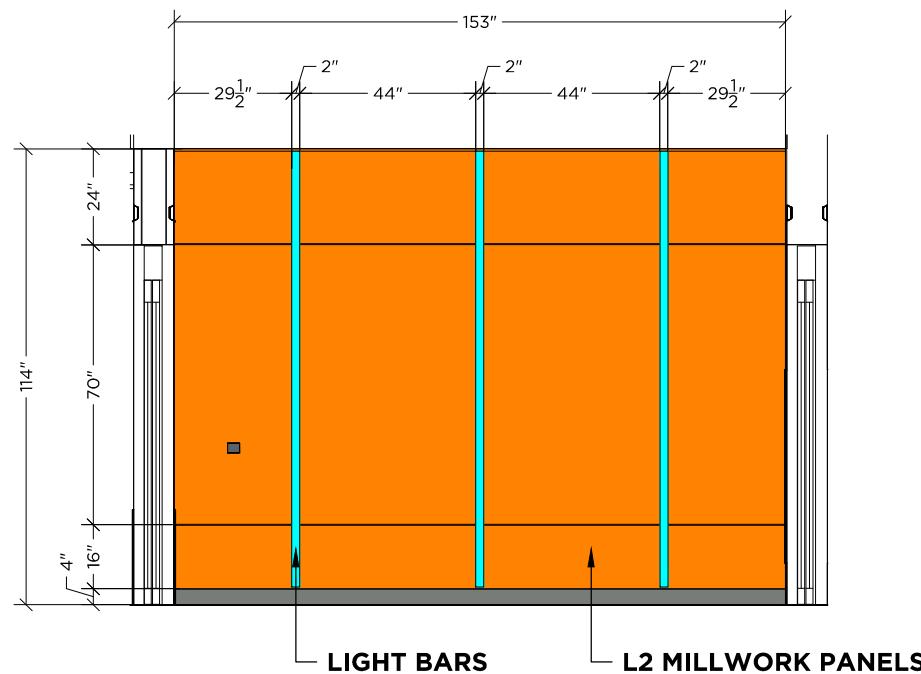


2 LOCKER ENTRY WEST | 1.2.1
SCALE: 1/4" = 1'-0"

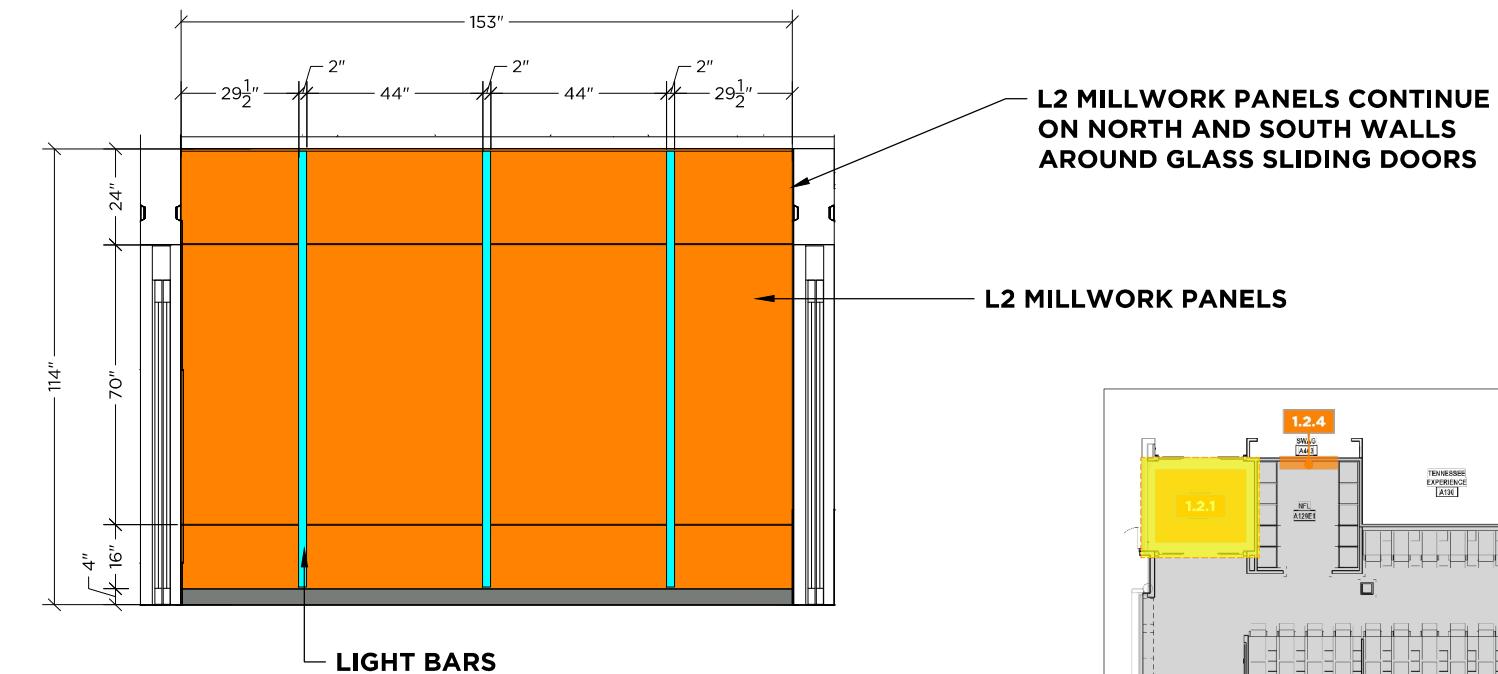


3 LOCKER ENTRY EAST | 1.2.1
SCALE: 1/4" = 1'-0"

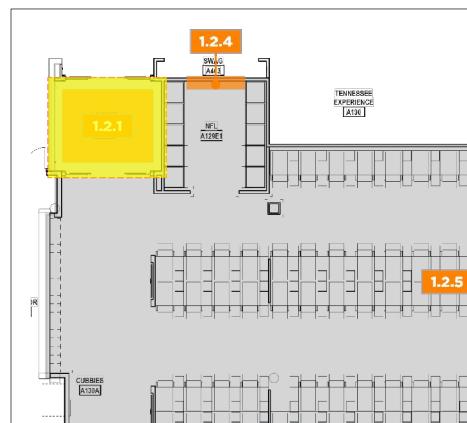

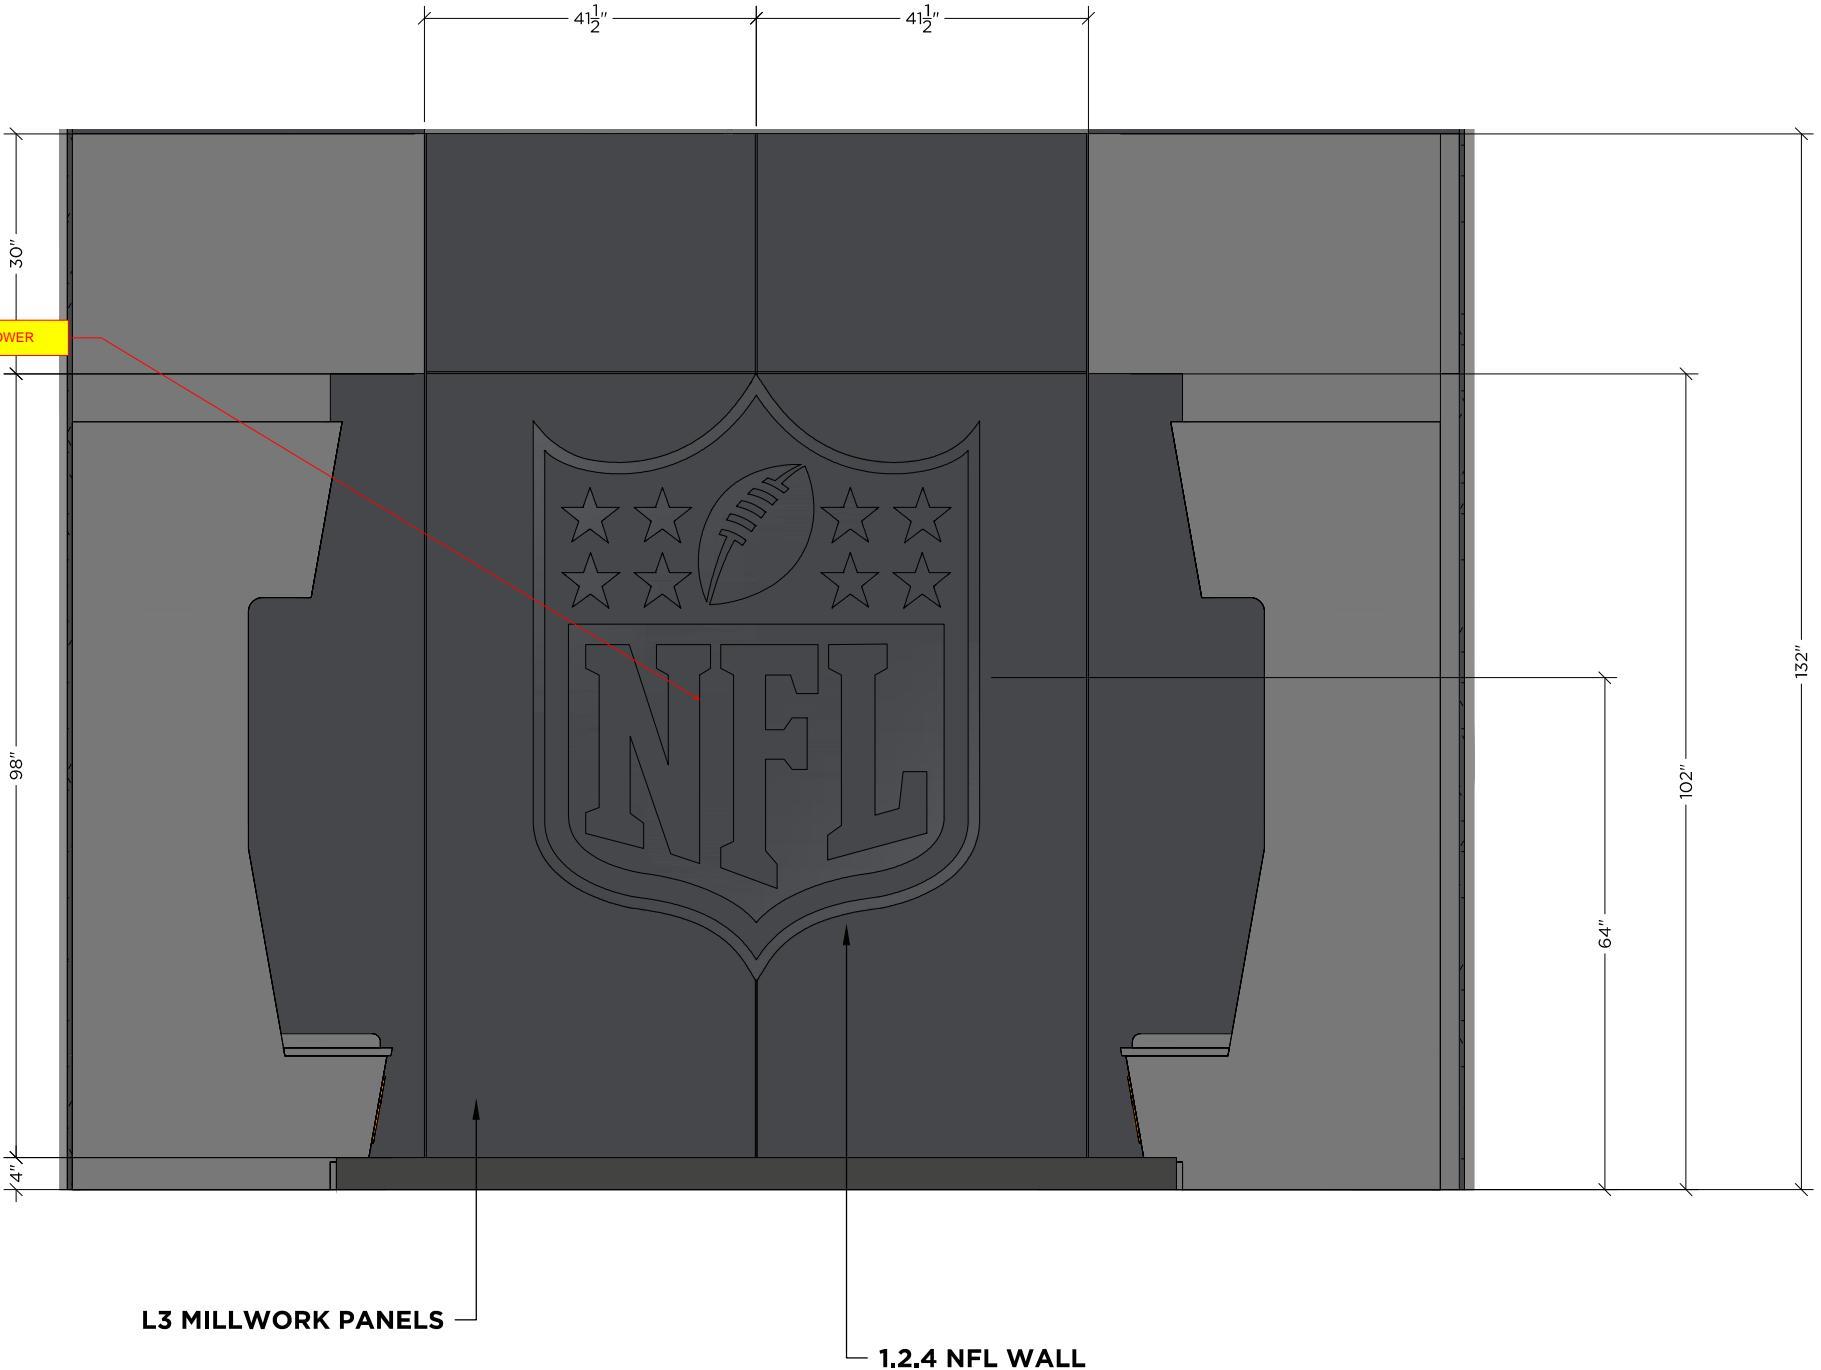

1 NFL WALL - NORTH 1.2.4
SCALE: 1/2" = 1'-0"



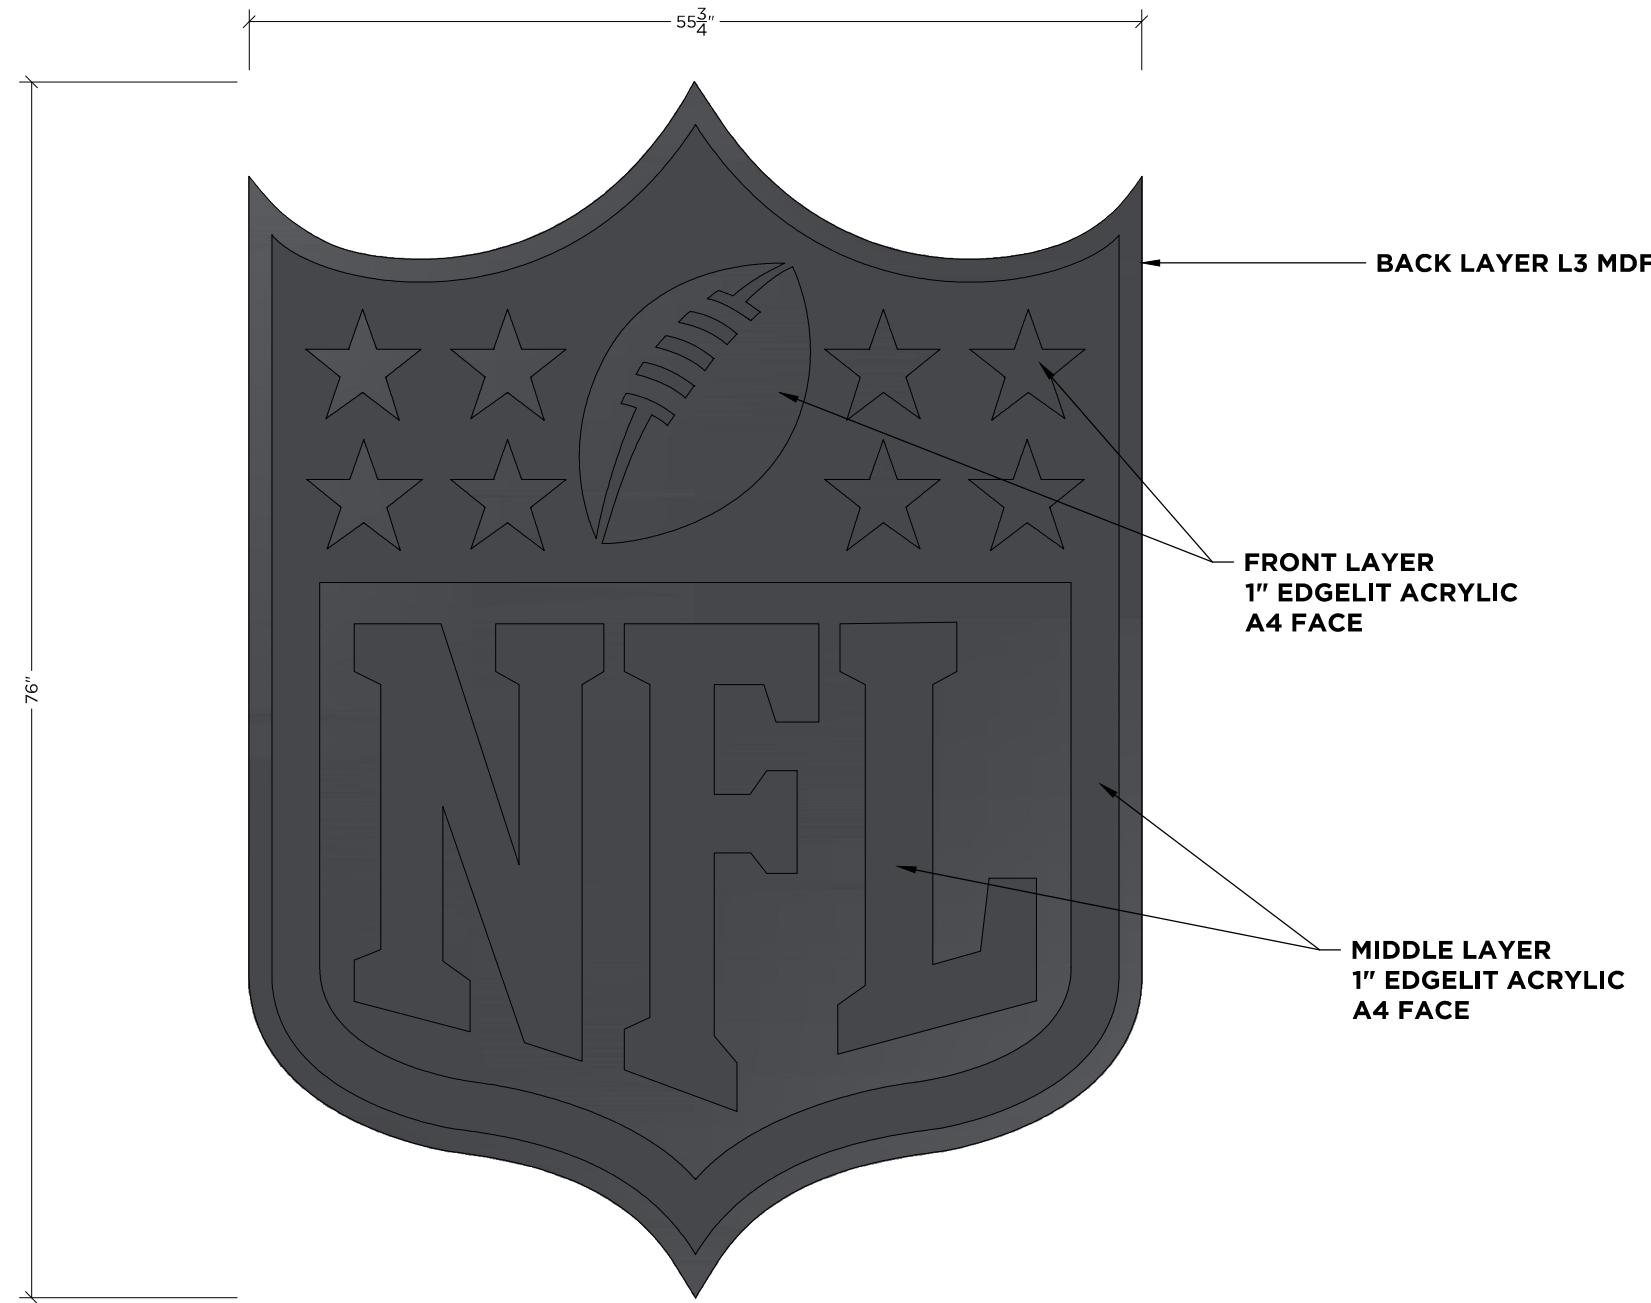

1 NFL WALL LOGO 1.2.4
SCALE: 1" = 1'-0"